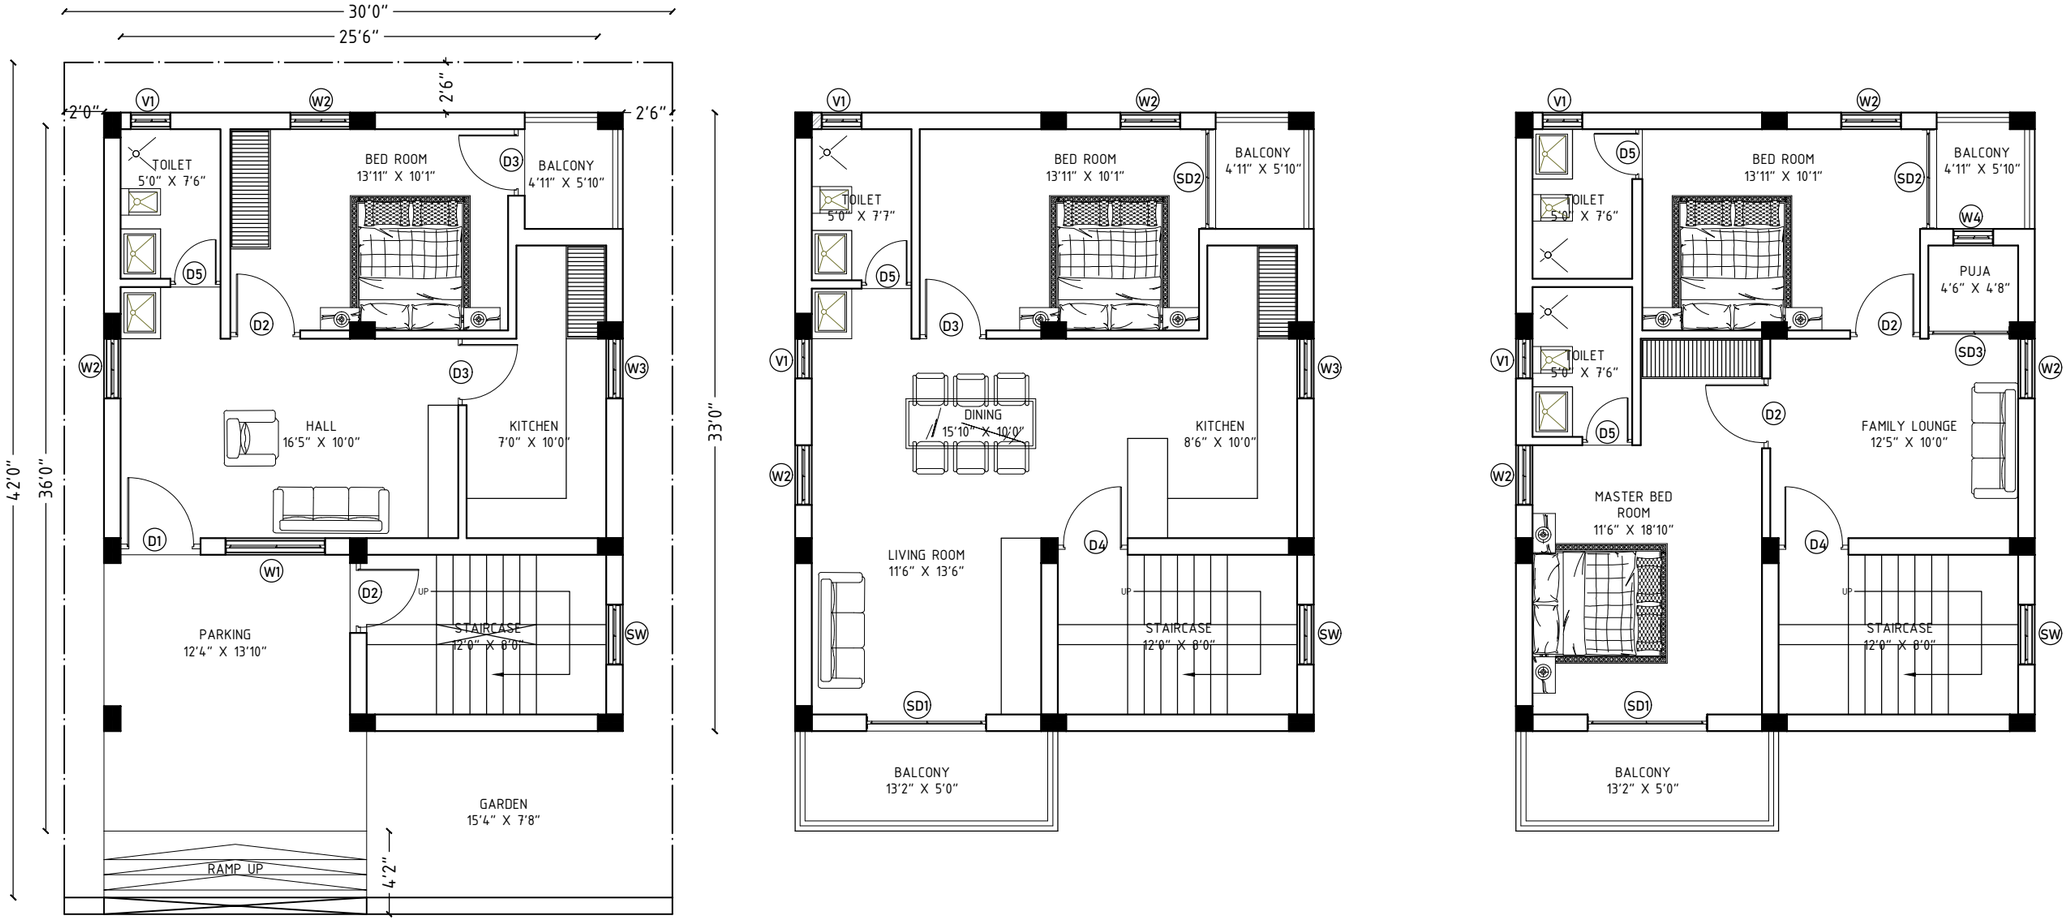

NOTES

1. THIS DRAWING IS THE PROPERTY OF THE ADCO VENTURES PRIVATE LIMITED AND IS NOT TO BE USED OR REPRODUCED WITHOUT THEIR PRIOR PERMISSION.
2. DRAWING IS NOT TO BE SCALED. ONLY WRITTEN DIMENSIONS ARE TO BE FOLLOWED.
3. ANY DEVIATION OR CHANGES SHOULD BE REFFERED TO THE ARCHITECTS.

DOOR SCHEDULE

SL.	NAME	SIZE	SILL	LINTEL
1.	D1	4' X 7'		7'
2.	D2	3'6" X 7'		7'
3.	D3	3'4" X 7'		7'
4.	D4	3'1" X 7'		7'
5.	D5	2'6" X 7'		7'
6.	SD1	6' X 7'		7'
7.	SD2	5' X 7'		7'
8.	SD3	4'1" X 7'		7'

WINDOW SCHEDULE

SL.	NAME	SIZE	SILL	LINTEL
1.	W1	5' X 4'6"	2'6"	7'
2.	W2	3' X 4'6"	2'6"	7'
3.	W3	3' X 4'	3'	7'
4.	W4	3' X 4'6"	2'6"	7'
5.	SW	3' X 4'6"		
6.	V1	3' X 3'	4'	7'

AREA STATEMENT
PLOT AREA-1260 Sq.Ft.
F.A.R. -2.00
GROUND FLOOR AREA- 844.5Sq.Ft.
FIRST FLOOR AREA- 840.5 Sq.Ft.
SECOND FLOOR AREA- 840.5 Sq.Ft.
TOTAL BUILTUP AREA- 2520 Sq.Ft.

ARCHITECT

ABHISHEK NR NAYAK
CA/2017/81449

APPLICANT

JOB TITLE

DRAWING TITLE
SOUTH FACING G+2 (30' X 42') FLOOR LAYOUT PLANS

SCALE	DRAWN BY	CHECKED BY
	SAGAR	ABHISHEK NR NAYAK CA/2017/81449

DRAWING NO.	SHEET NO.	NORTH
REVISION NO.	DATE 29-01-2021	

CONSULTANCY FIRM

ADCO VENTURES PRIVATE LIMITED
GROUND FLOOR, 2132/5124, NAGESWAR TANGI, BHUBANESWAR-751014, ODISHA, INDIA